




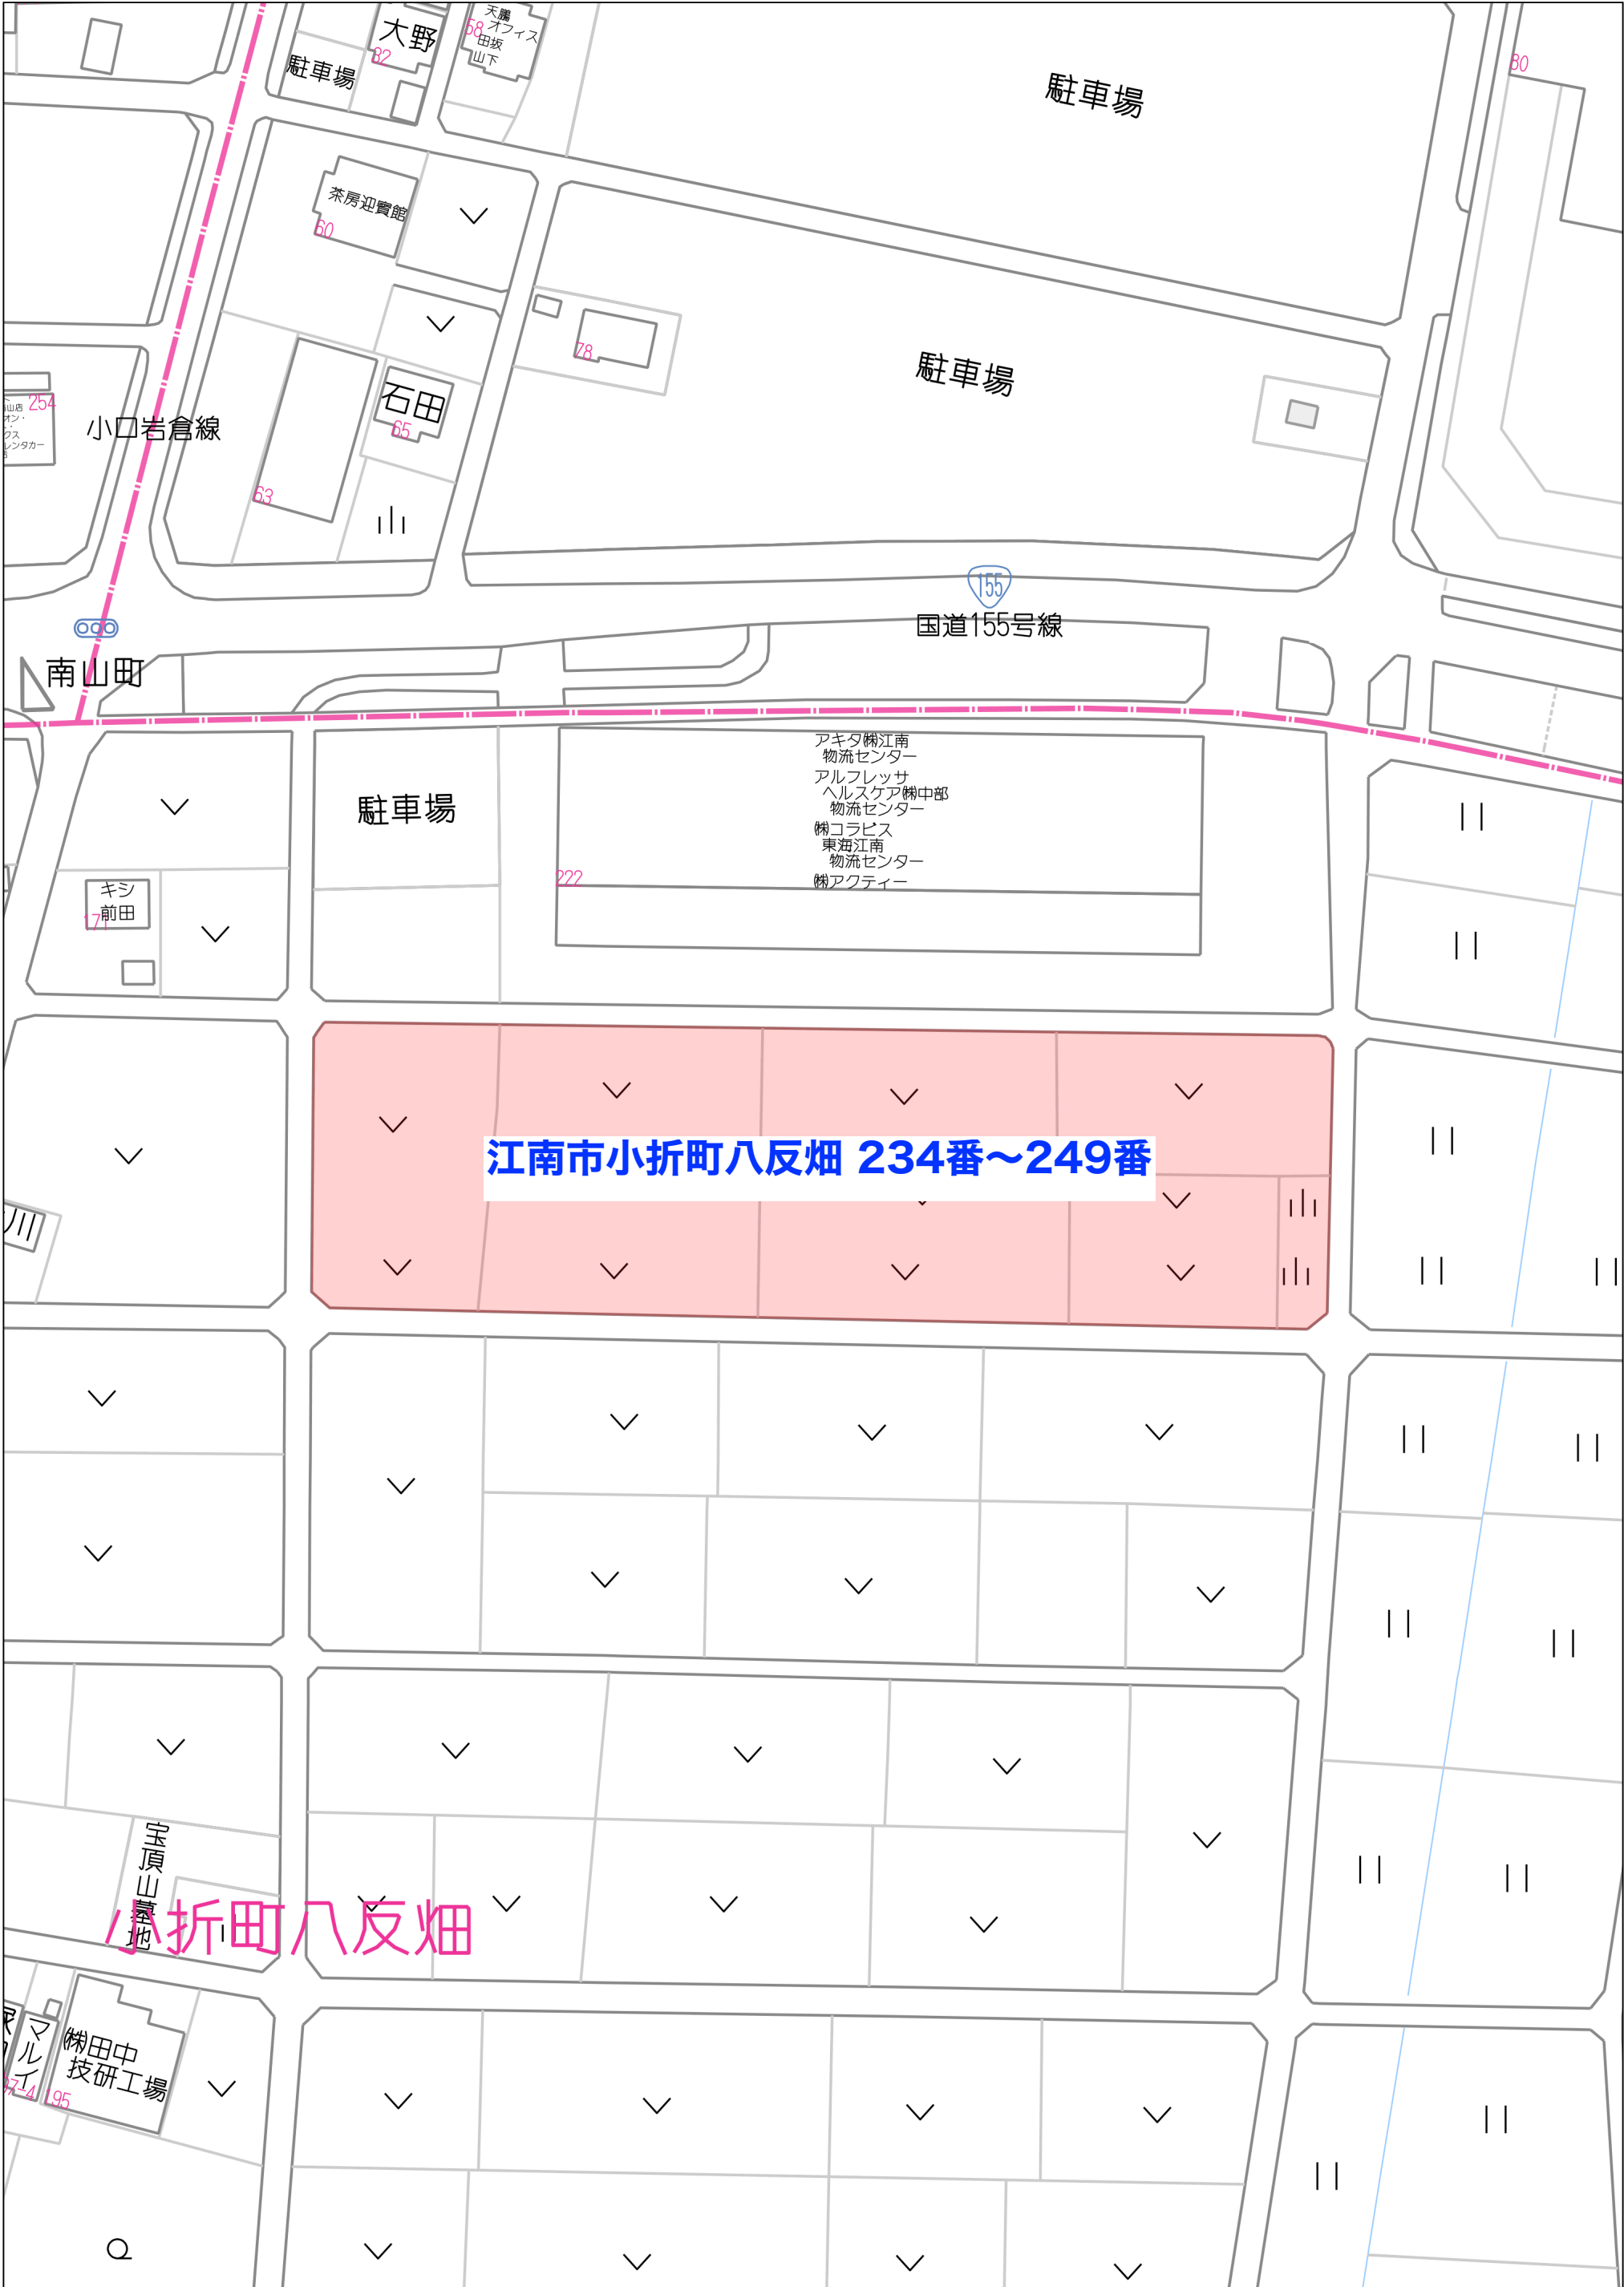

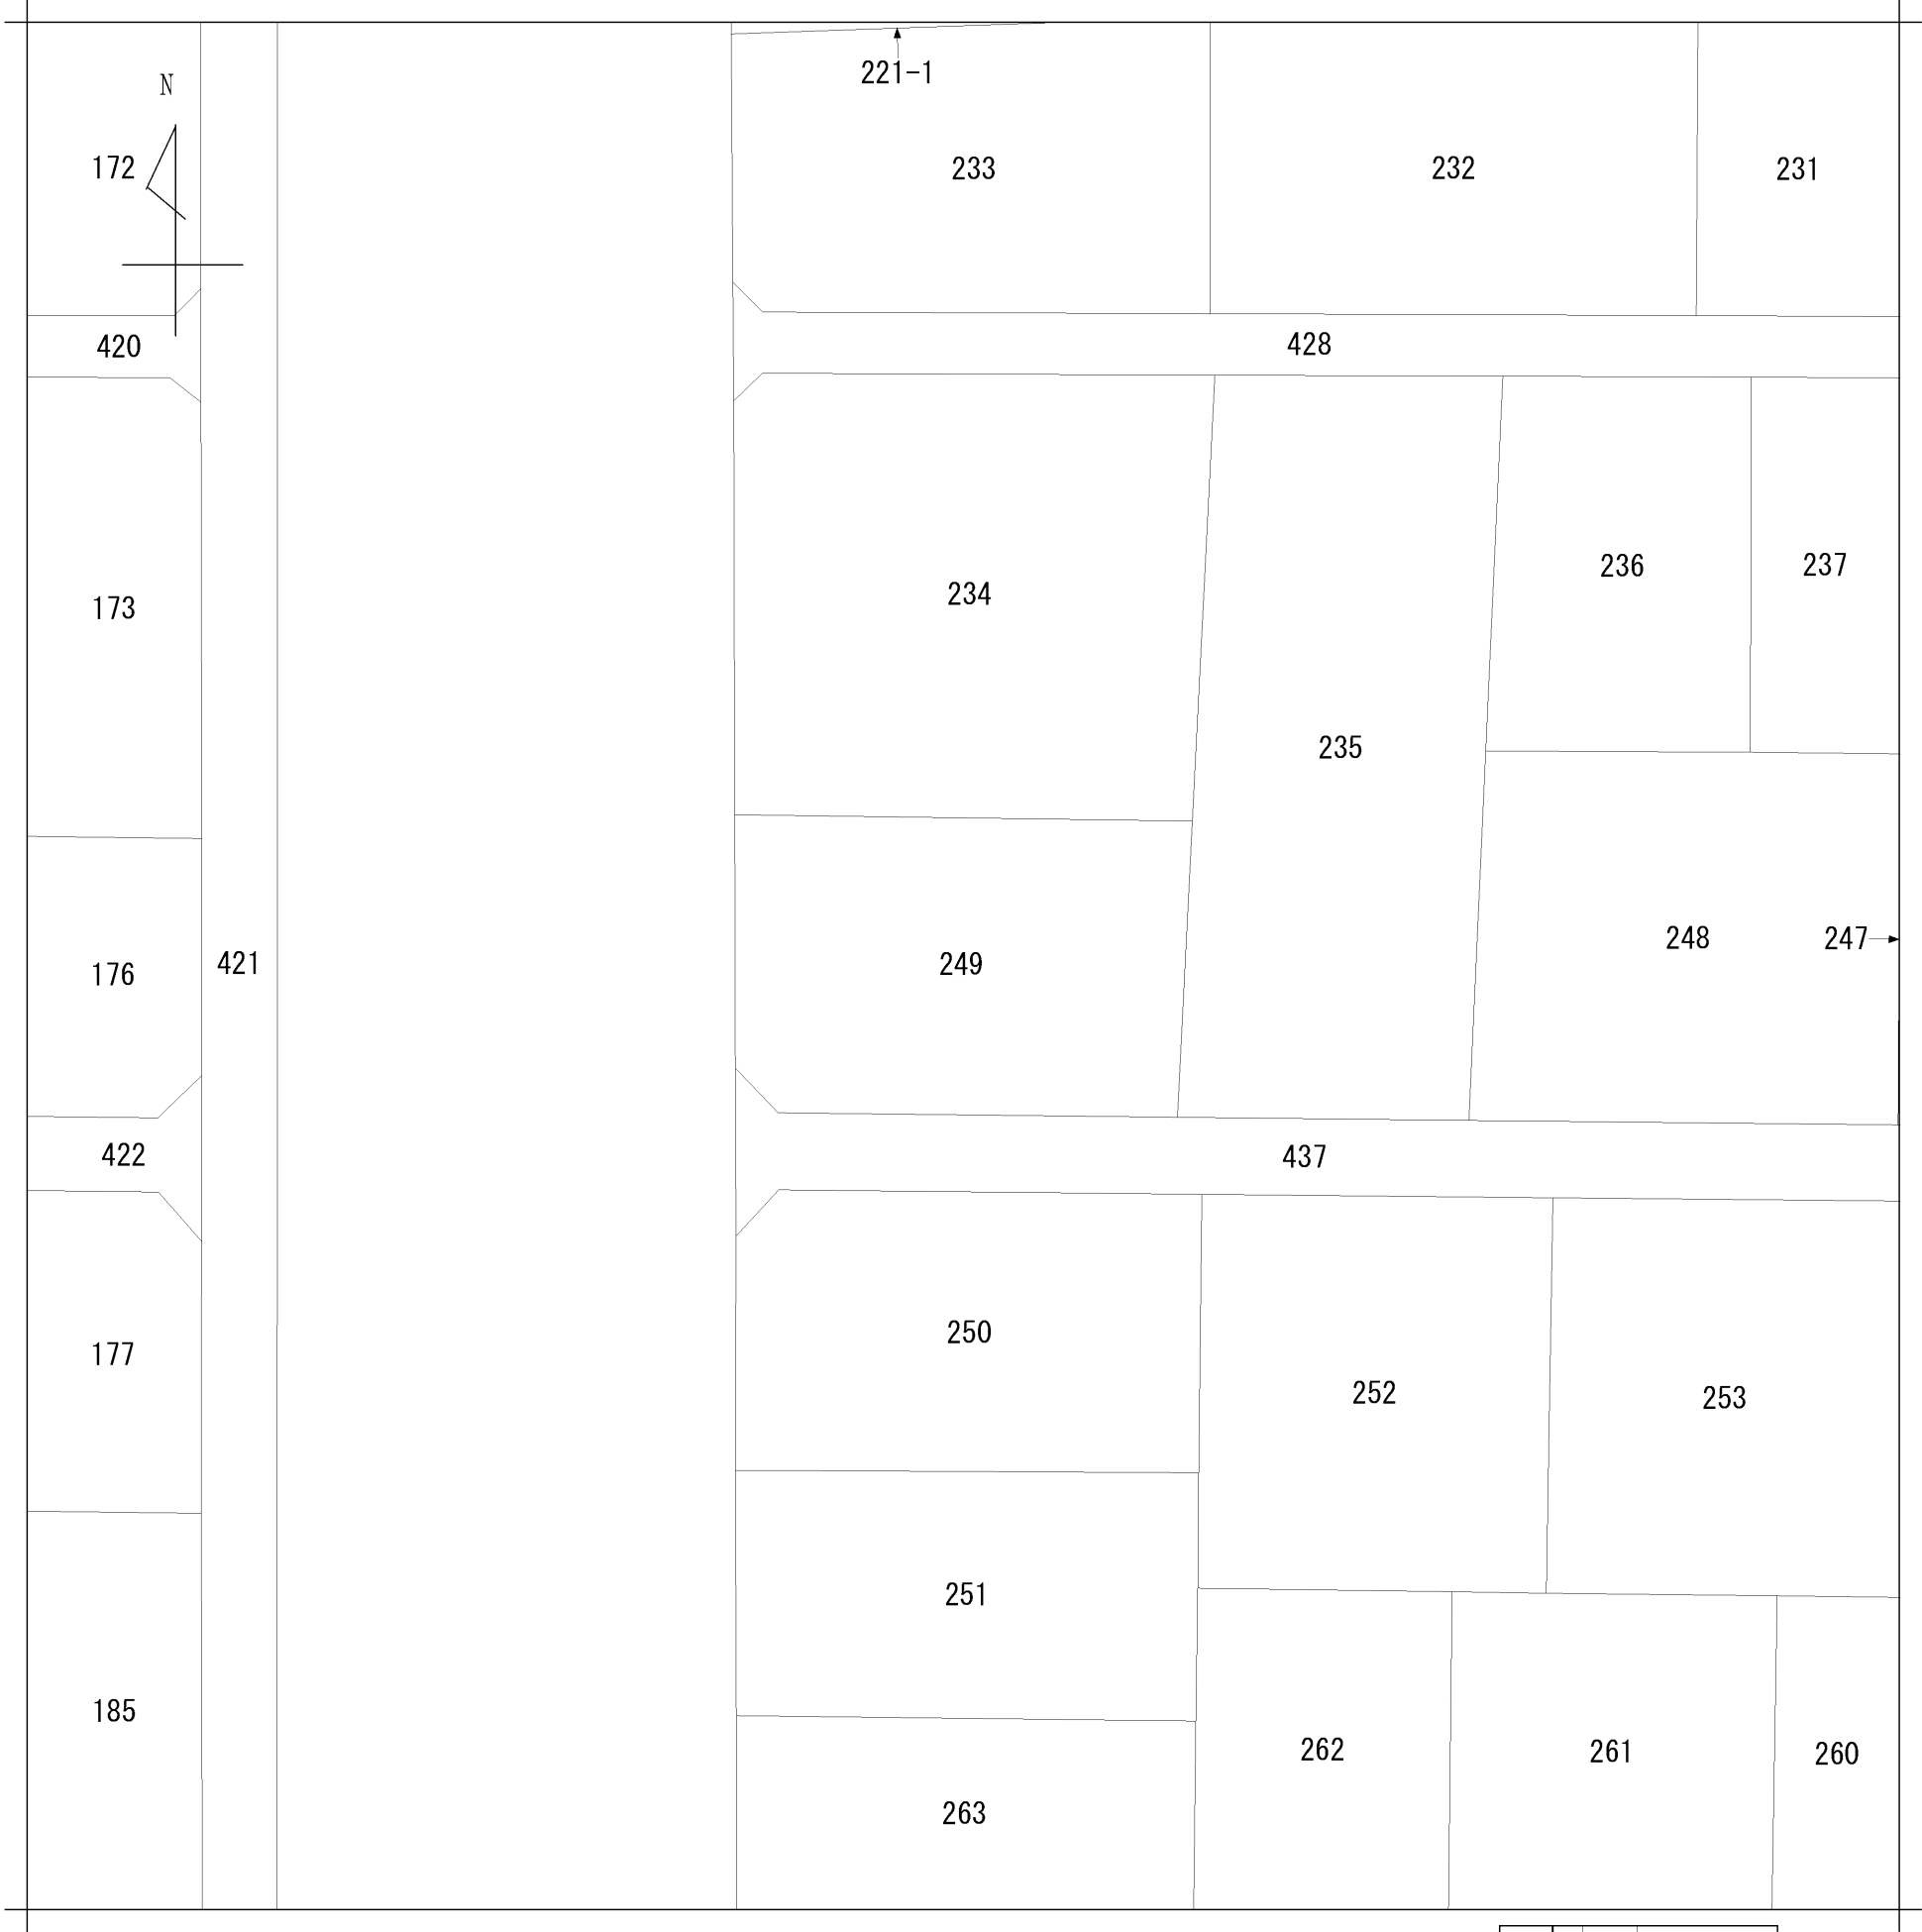


地番 区域見出	座標系 小折町八反畑	小折町 八反畑
------------	---------------	------------

請 求 部 分	所 在	江南市小折町八反畑					地 番	249番		
出 力 尺 縮	1/500	精 度 区 分	甲三	座 標 系 又 番 号 記 号		分 類	地図に準ずる図面		種 類	土地改良所在図
作 成 年 月 日	昭和61年10月21日				備 付 年 月 日 (原図)		補 事 記 項			

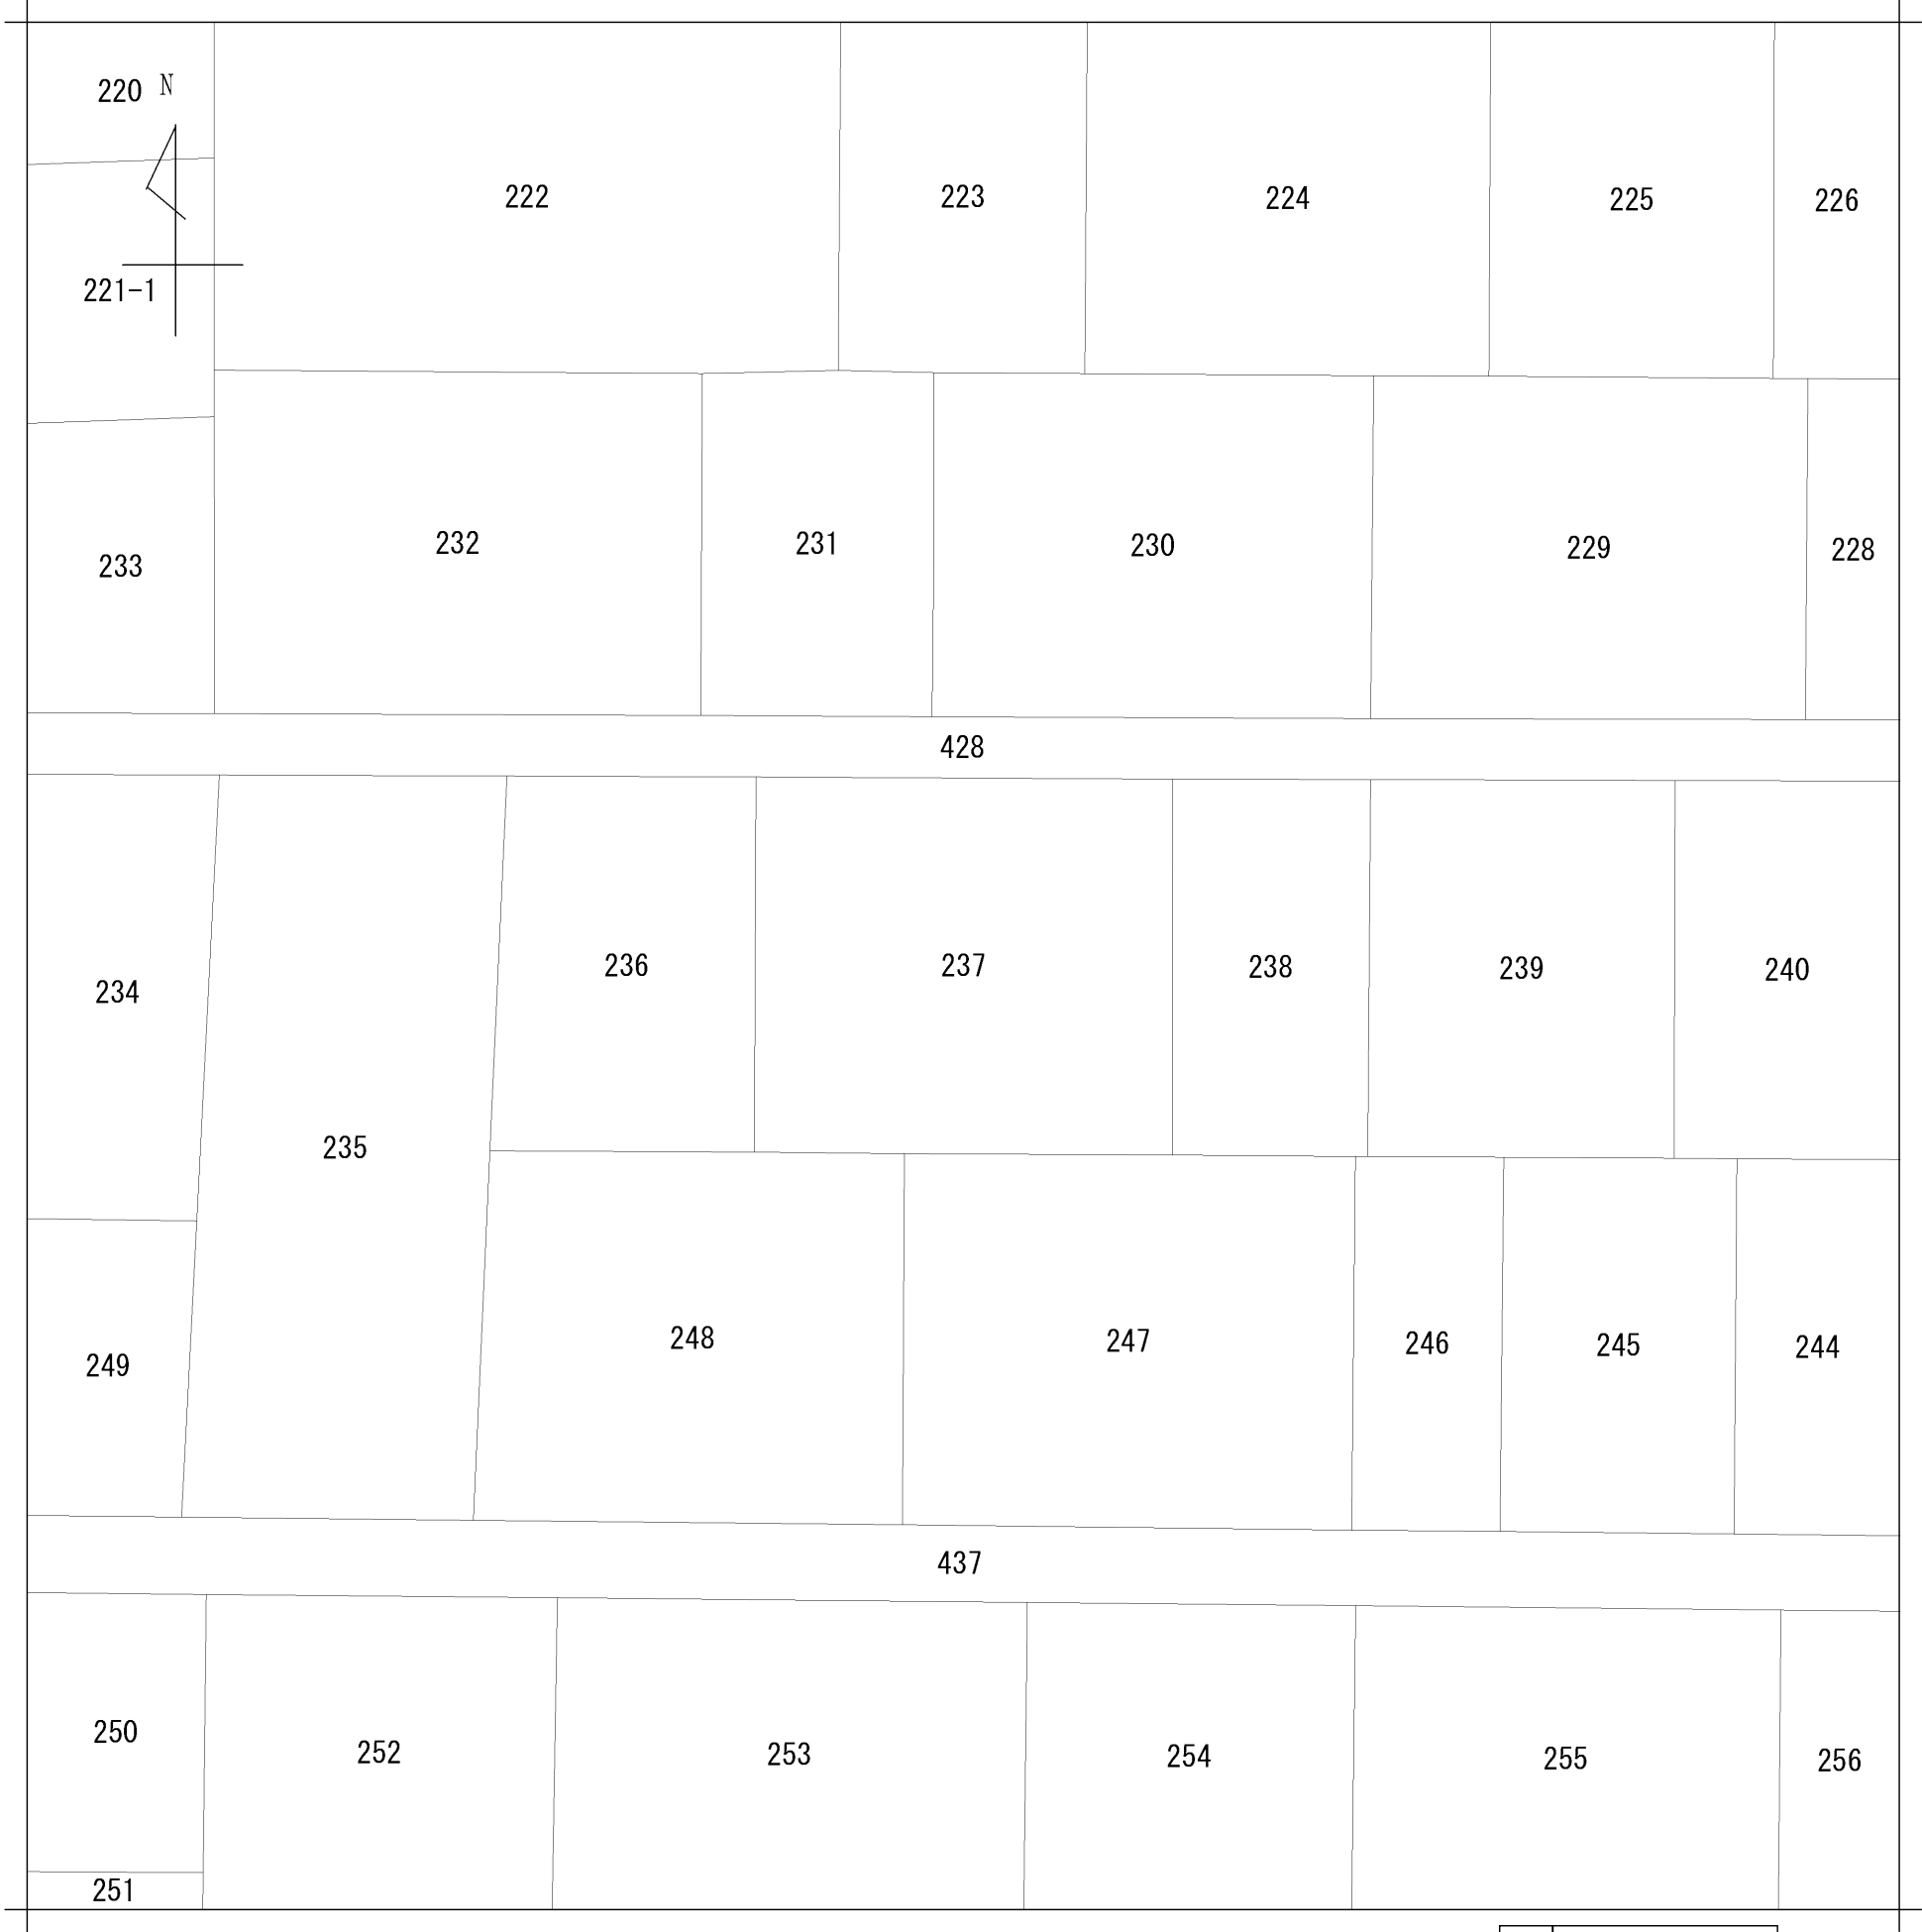

地番 区域見出	小折町八反畑
------------	--------

請 求 部 分	所 在	江南市小折町八反畑				地 番	237番			
出 力 縮 尺	1/500	精 度 区 分	甲三	座標系 番号又 は記号		分類	地図に準ずる図面		種類	土地改良所在図
作 成 年 月 日	昭和61年10月21日			備 付 年 月 日 (原図)				補 記 事 項		

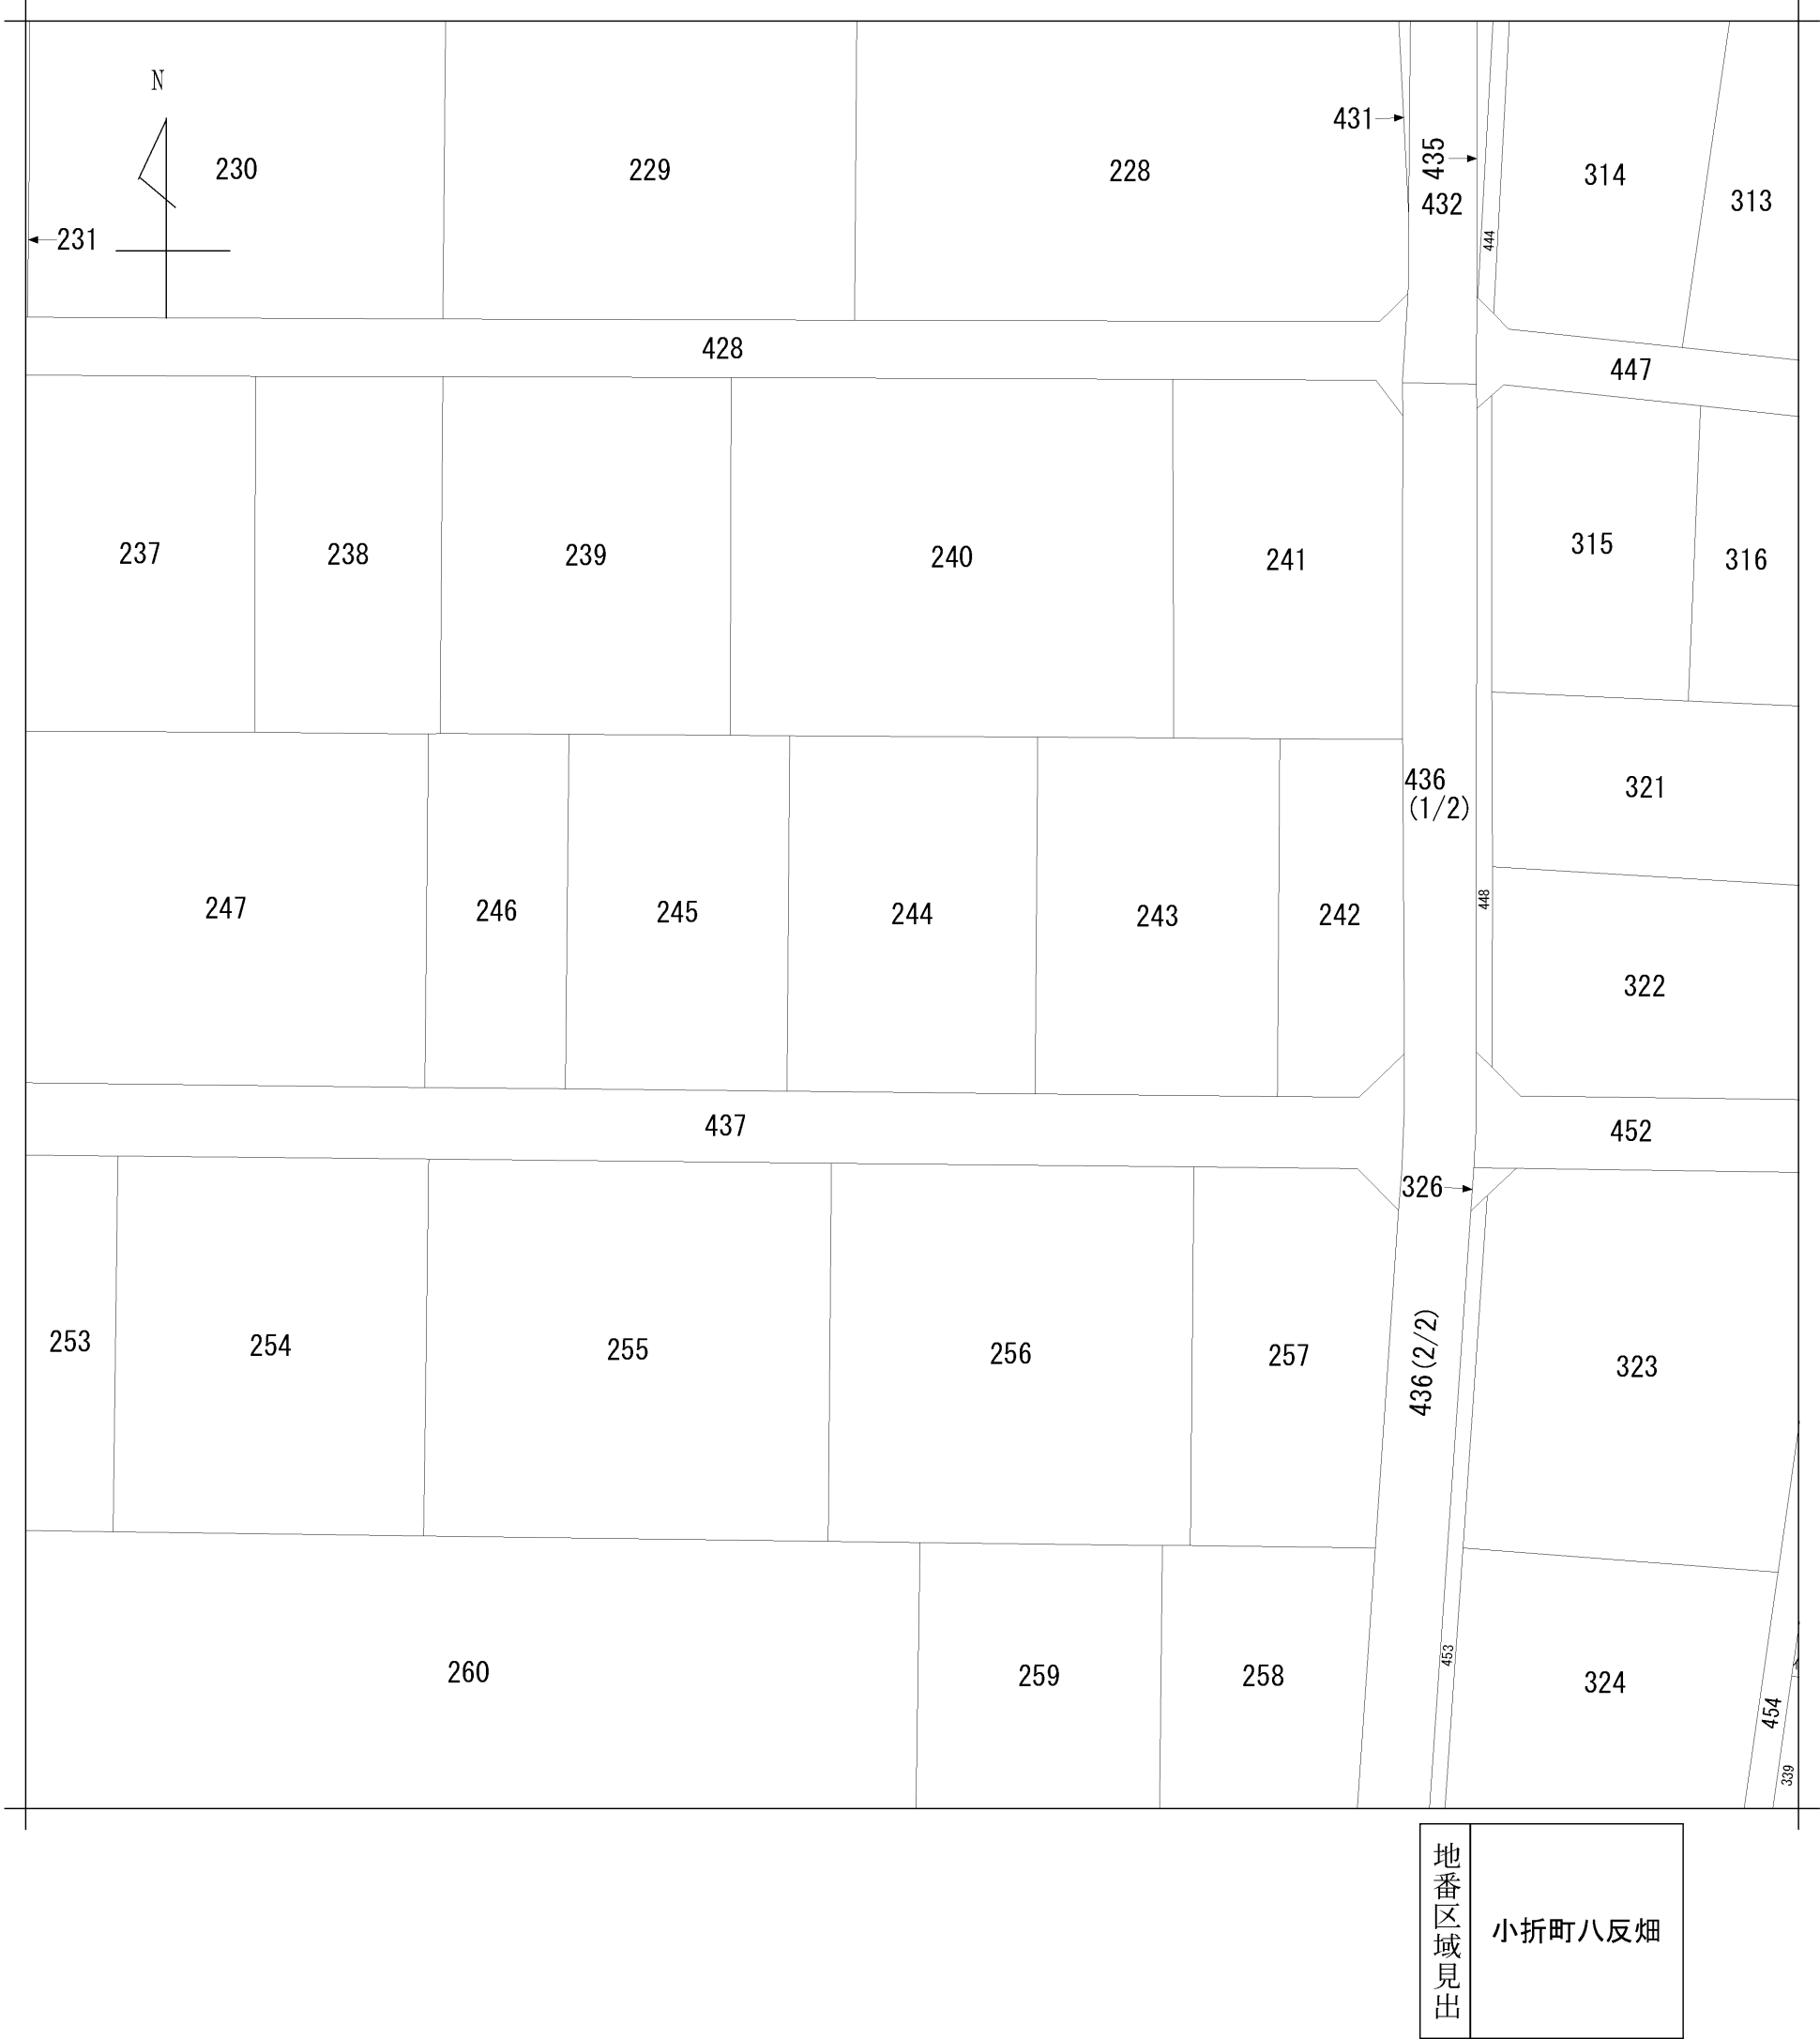

請 求 部 分	所 在	江南市小折町八反畑					地 番	244番			
出 縮 力 尺	1/500	精 度 区 分	甲三	座標系 番号又は 記号		分類	地図に準ずる図面			種類	土地改良所在図
作 成 年月日	昭和61年10月21日				備 付 年月日 (原図)				補 記 事 項		